


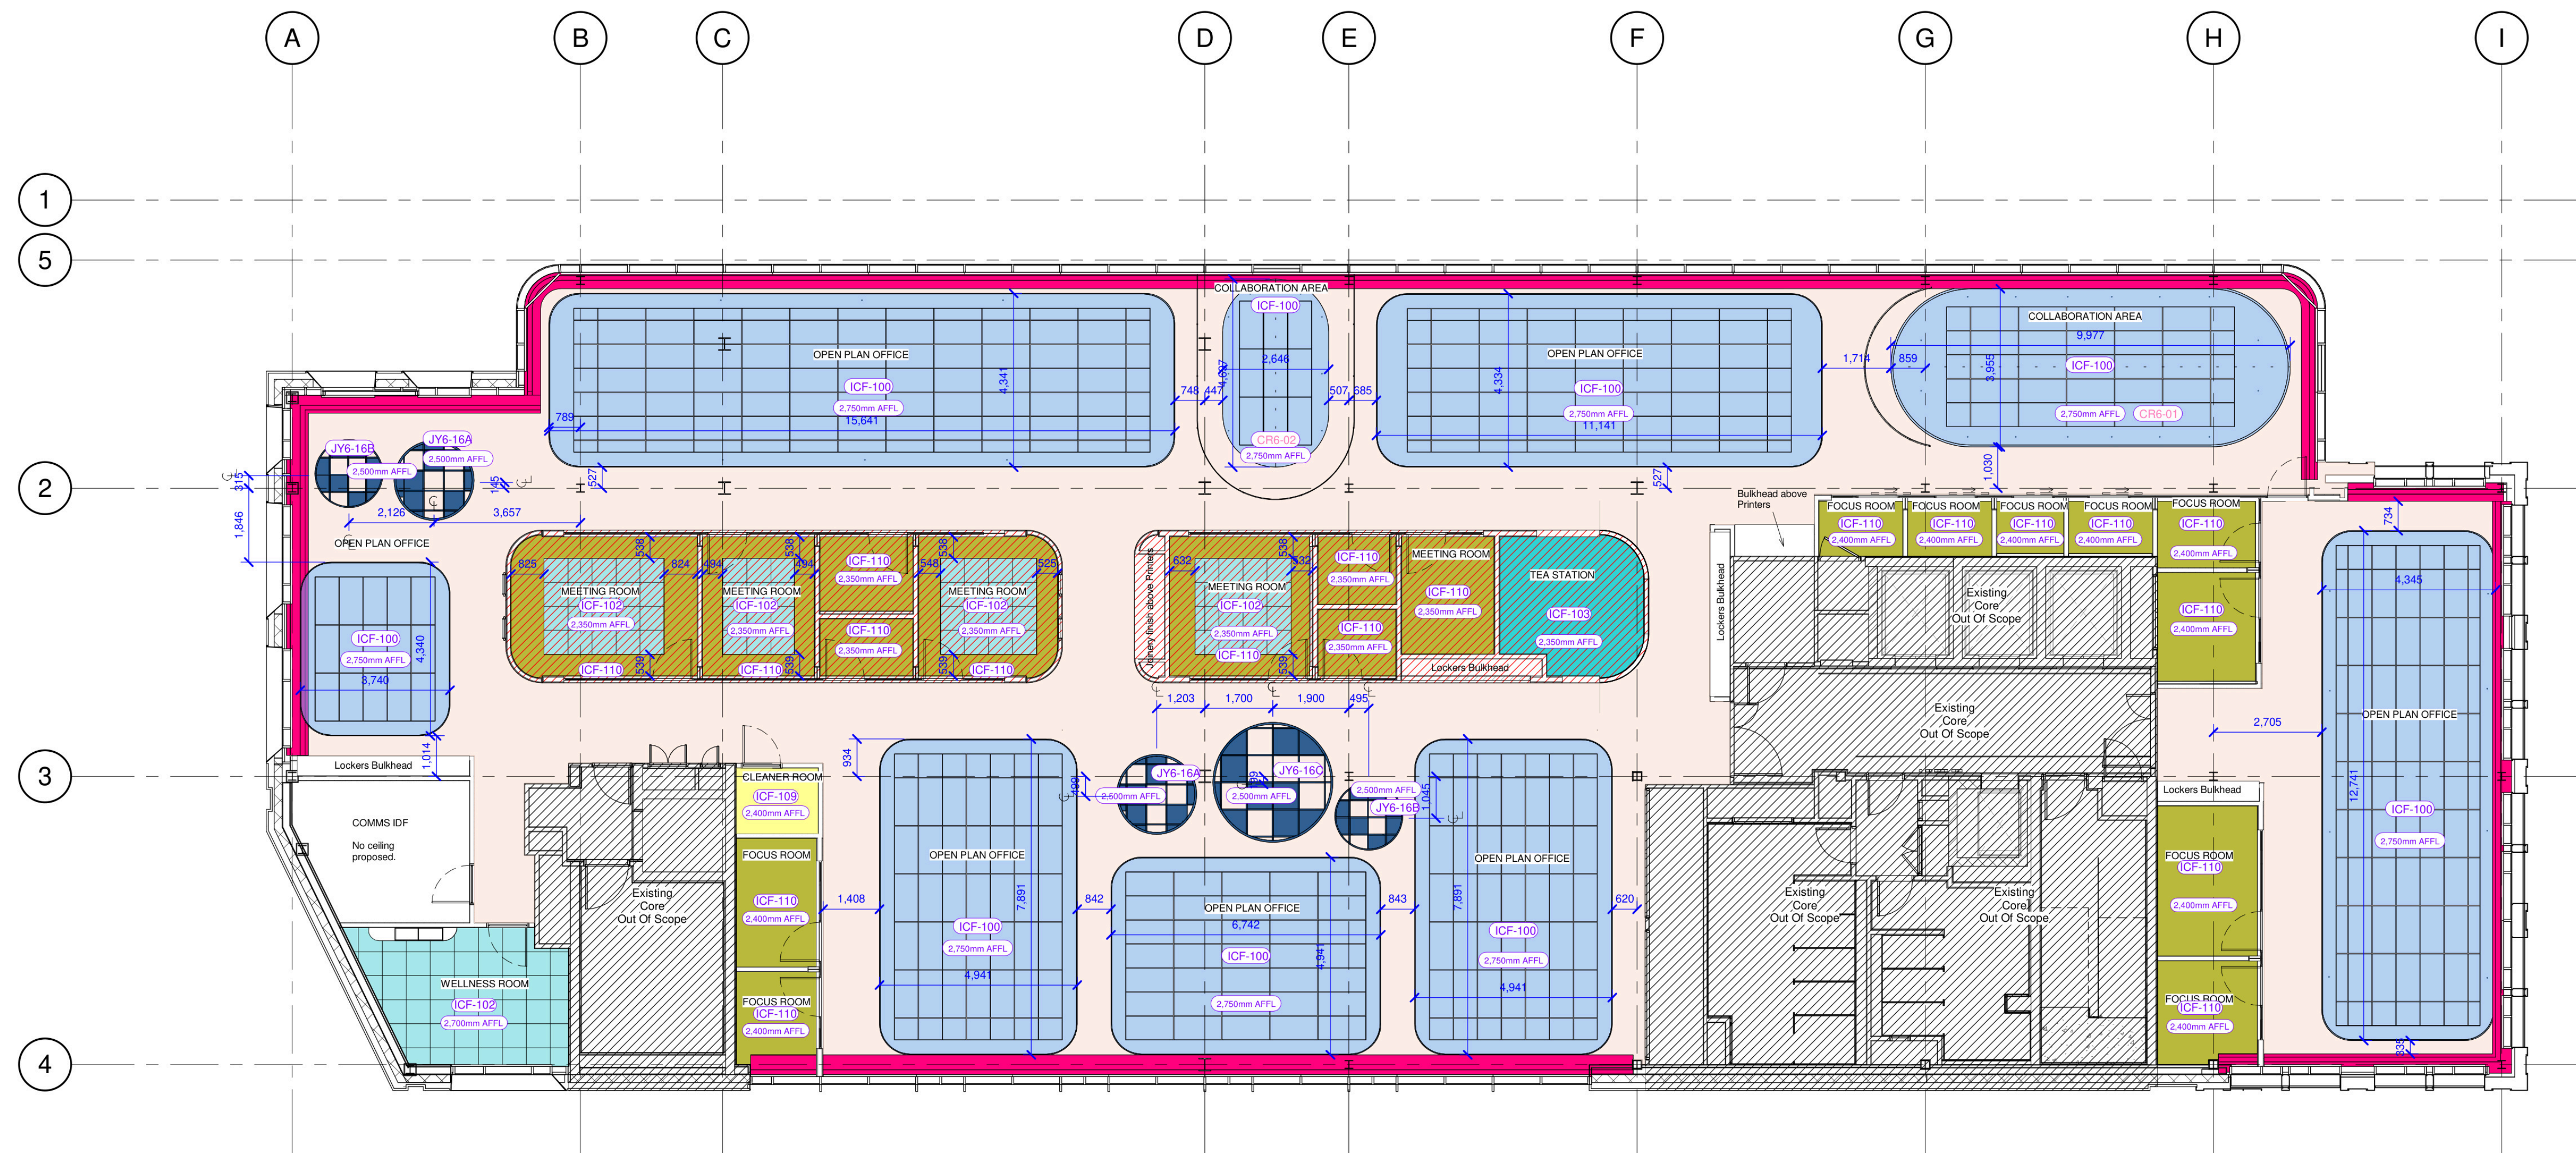

1 L06 - Sixth Floor Reflected Ceiling Plan
1 : 100

Notes:

Drawing Notes:

- General Note:
1. Shop Drawing to be approval/sign off before construction.
 2. All existing dimensions including any loose fit, are to be brought to the locations with reference to the existing structure.
 3. All switch points are to be approved by the architect.
 4. All drawings to be in accordance with the architect's drawings and present.
 5. Samples for all finishes to be provided by the architect.
 6. Part samples as required by the architect.
 7. Stability of the unit: contractor/joiner.
 8. Please read all drawings and schedules issued as part of the contract.
 9. Joiner to conduct the work.
 10. Part samples to be provided by the contractor.
 11. All timber/mdf to be finished with a clear coat.

CEILING FINISH

ICF-100	ICF-100
ICF-102	ICF-102
ICF-103	ICF-103
ICF-106	ICF-106
ICF-107	ICF-107
ICF-108	ICF-108
ICF-109	ICF-109
ICF-110	ICF-110
ICF-111	ICF-111

Central spin skin and 17' steel support RAU-IA-70C detail.