




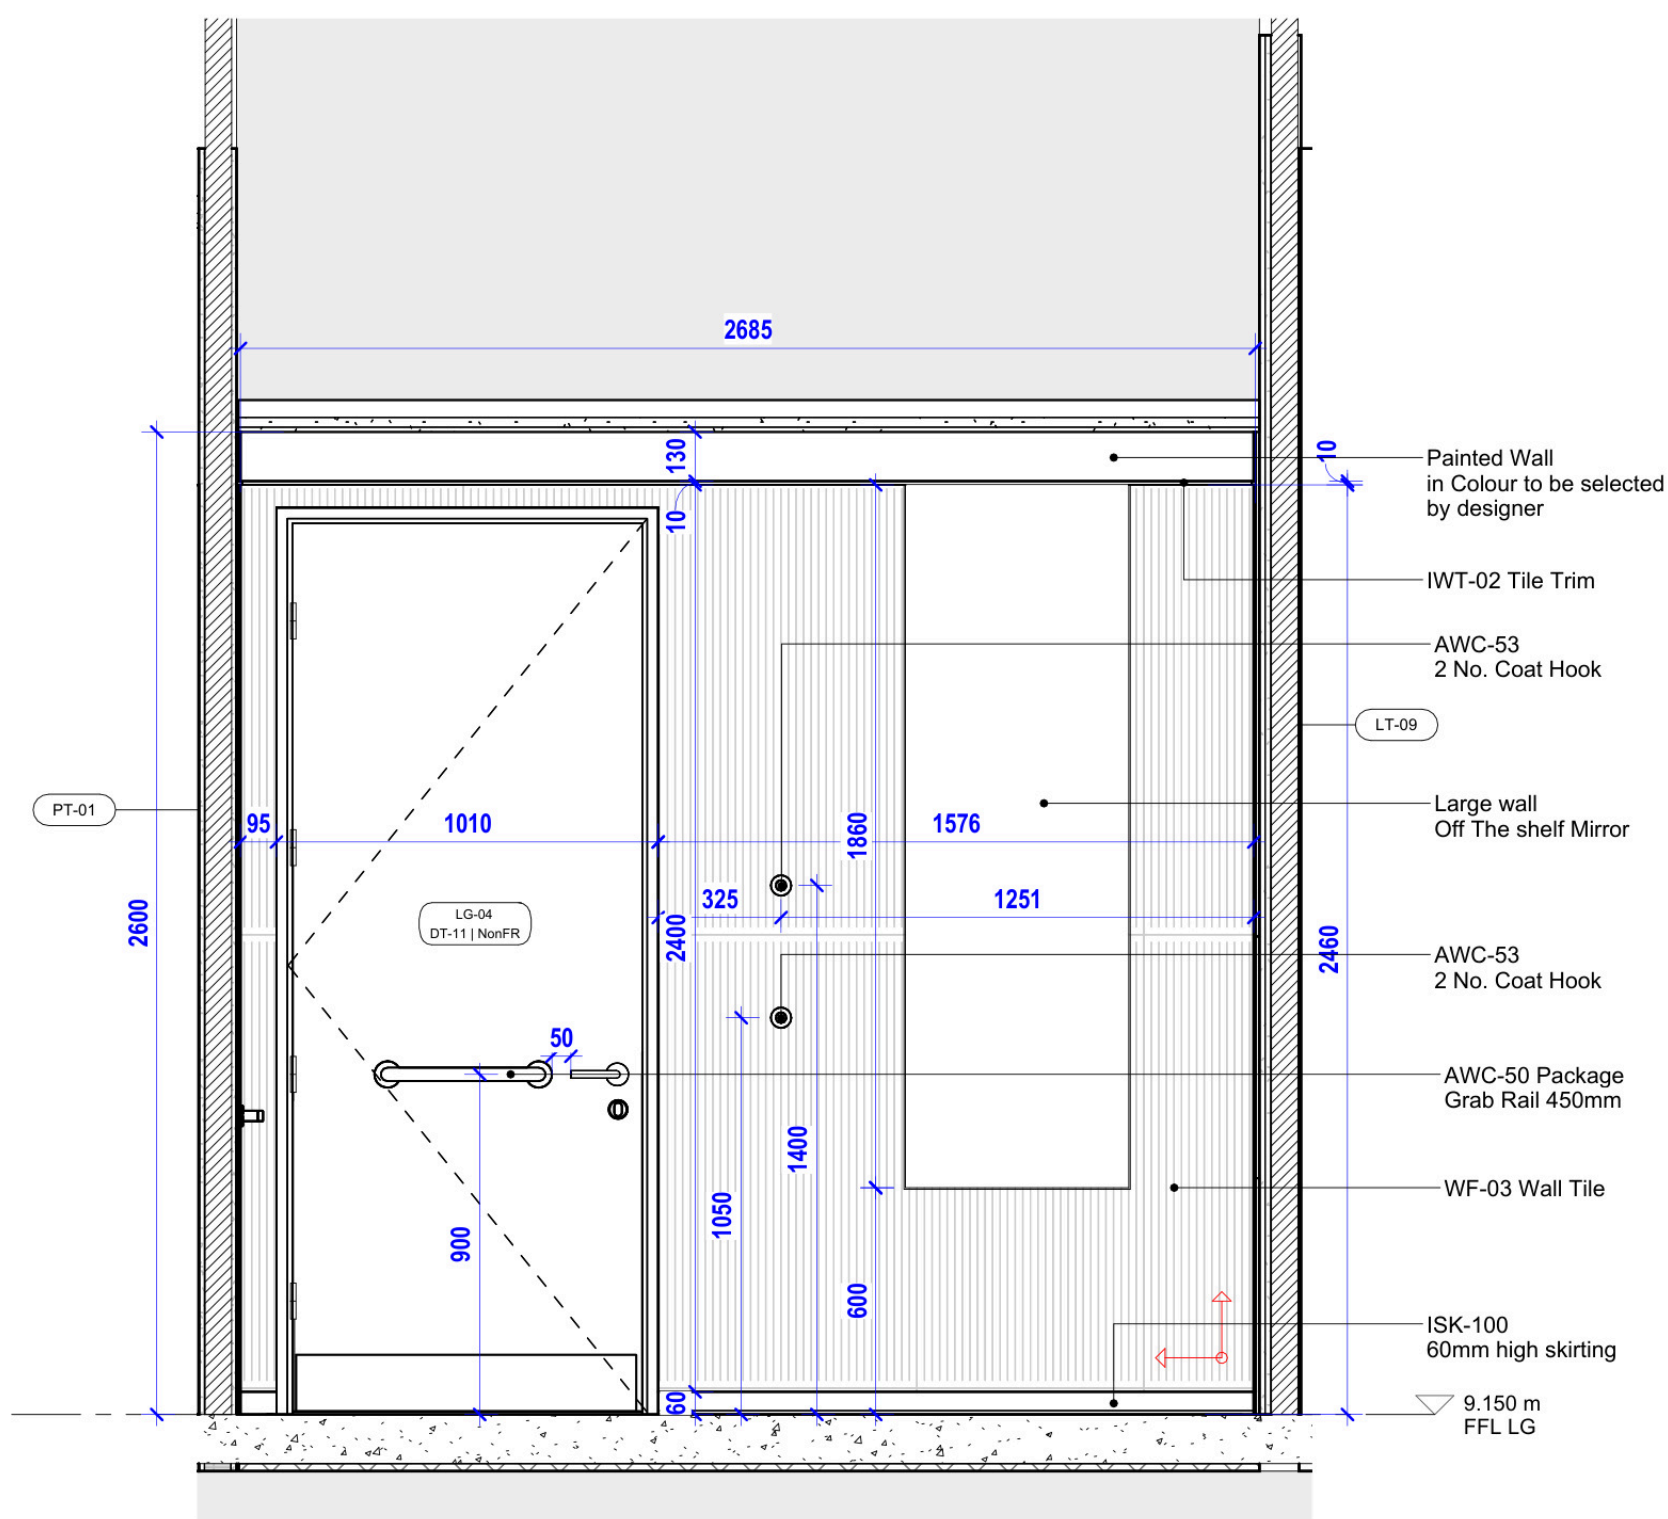


Male WC Elevation -b2
1 : 20

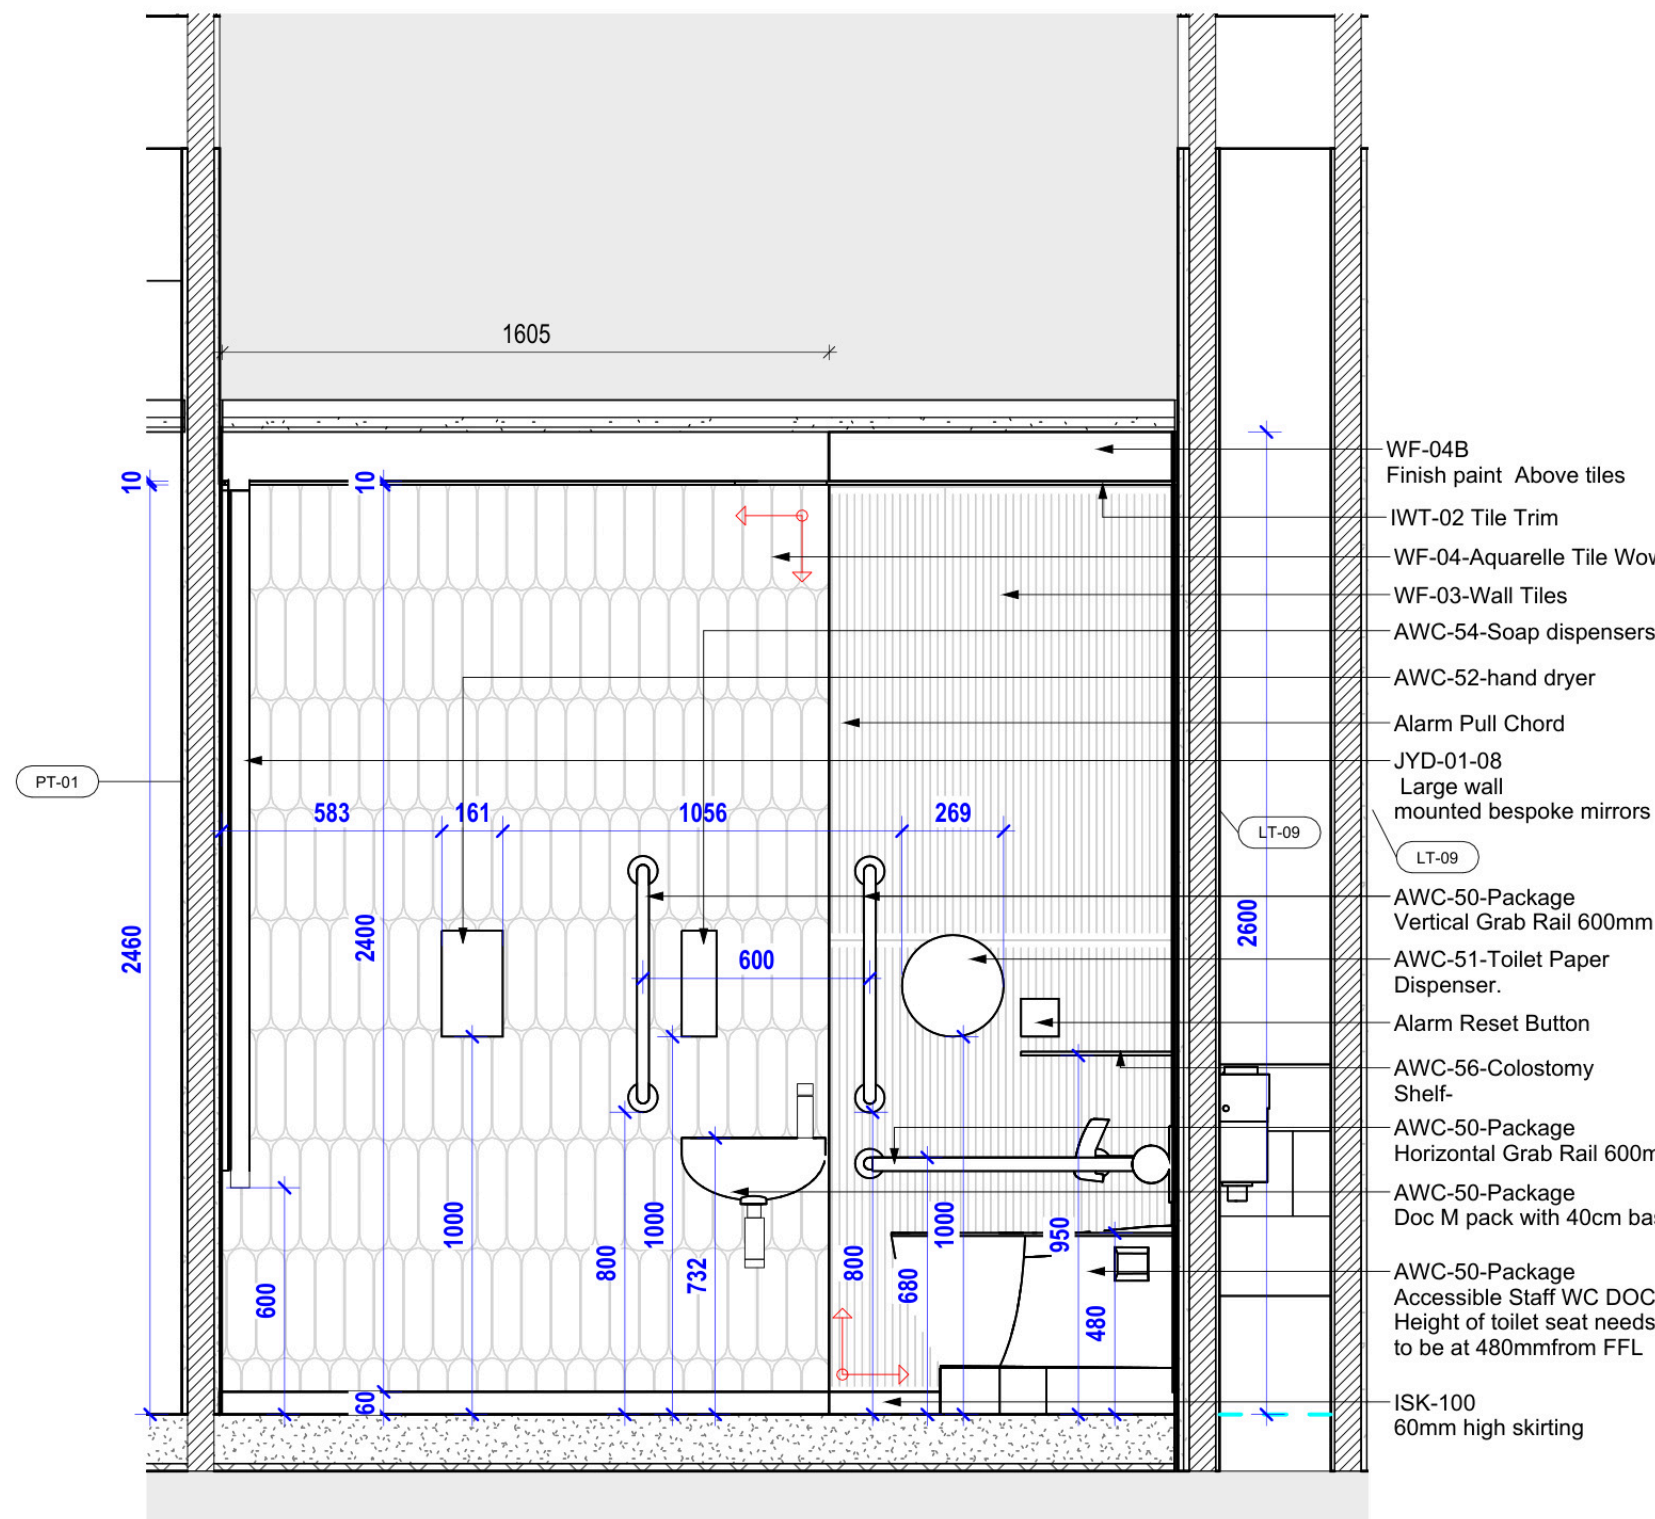


Ambulant Shower & WC Elevation -c1
1 : 20

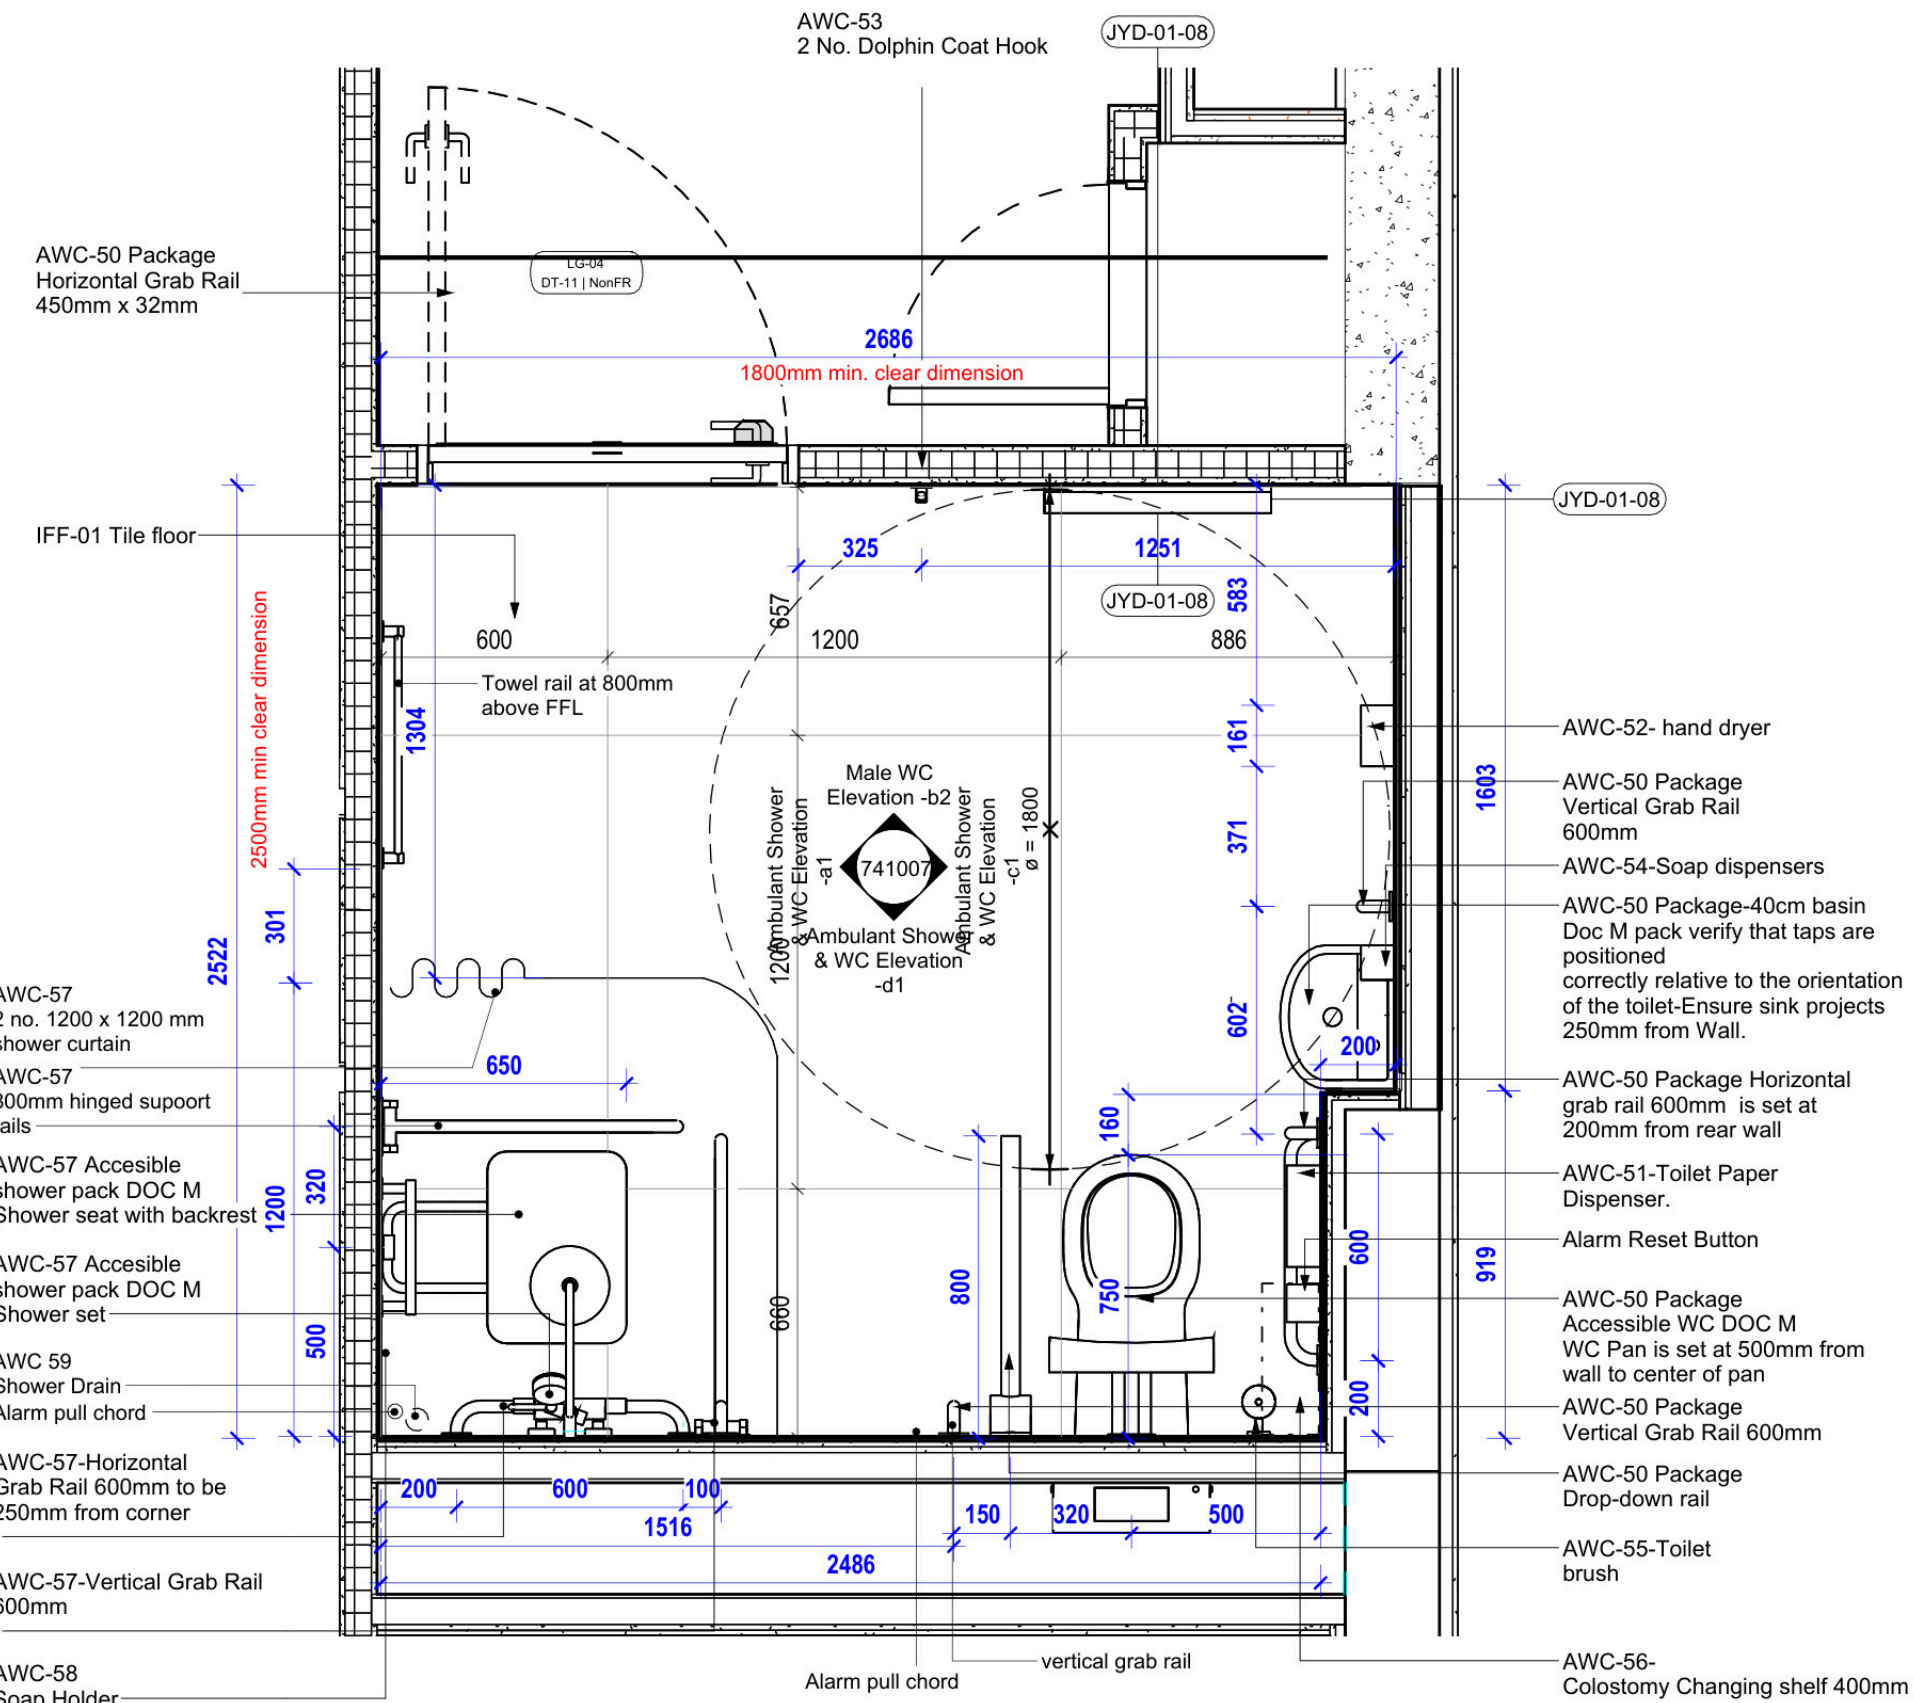


Ambulant Shower & WC Plan Basement -1
1 : 20

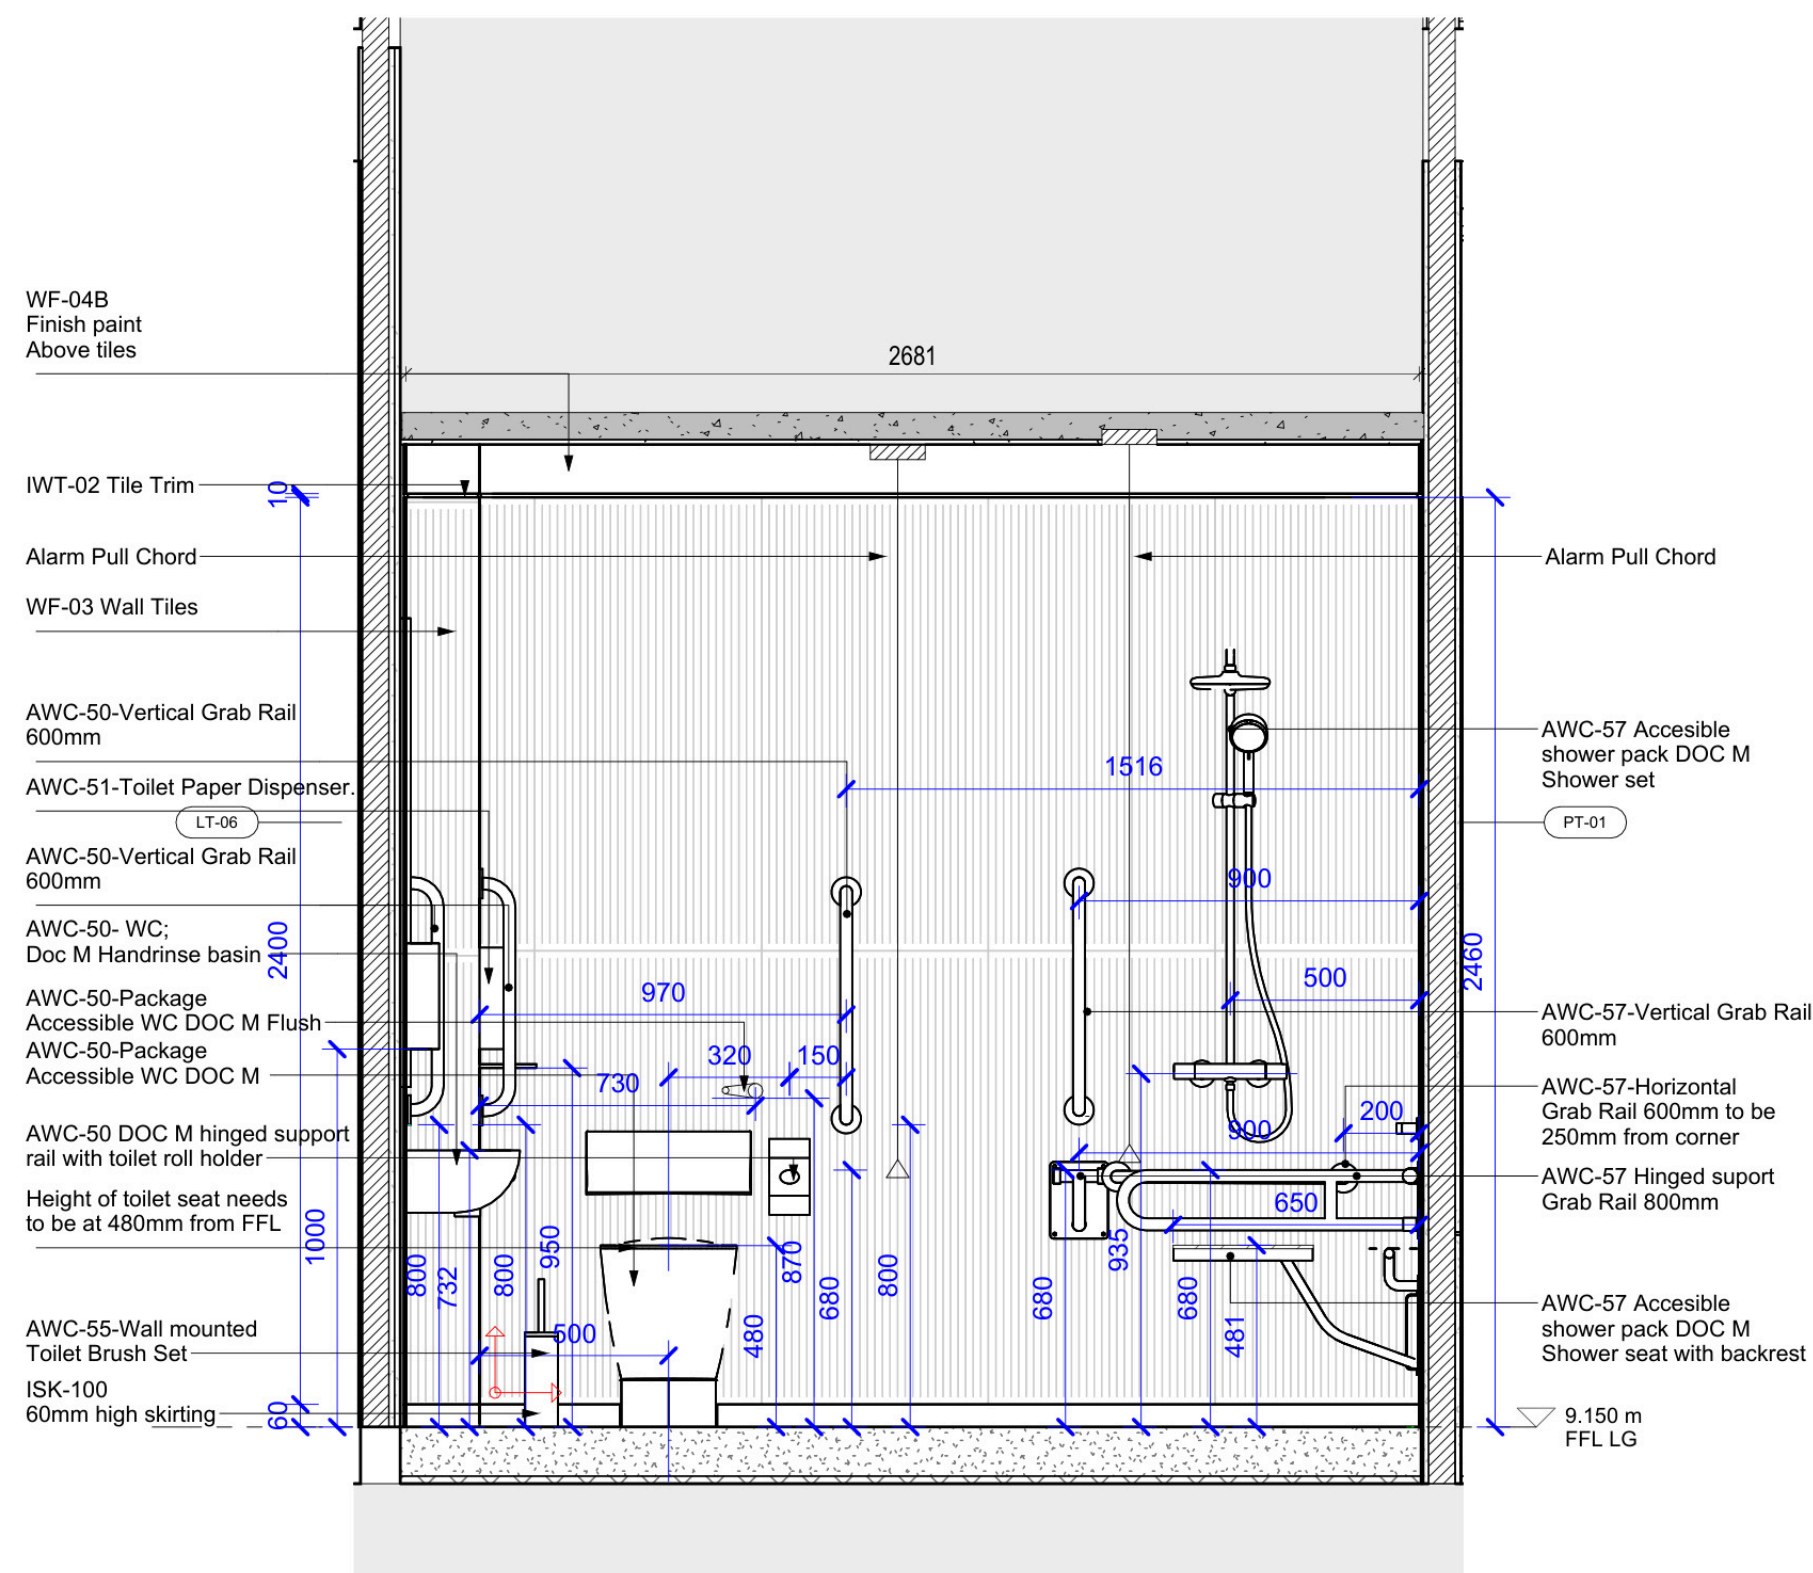

Ambulant Shower & WC Elevation -d1
1 : 20

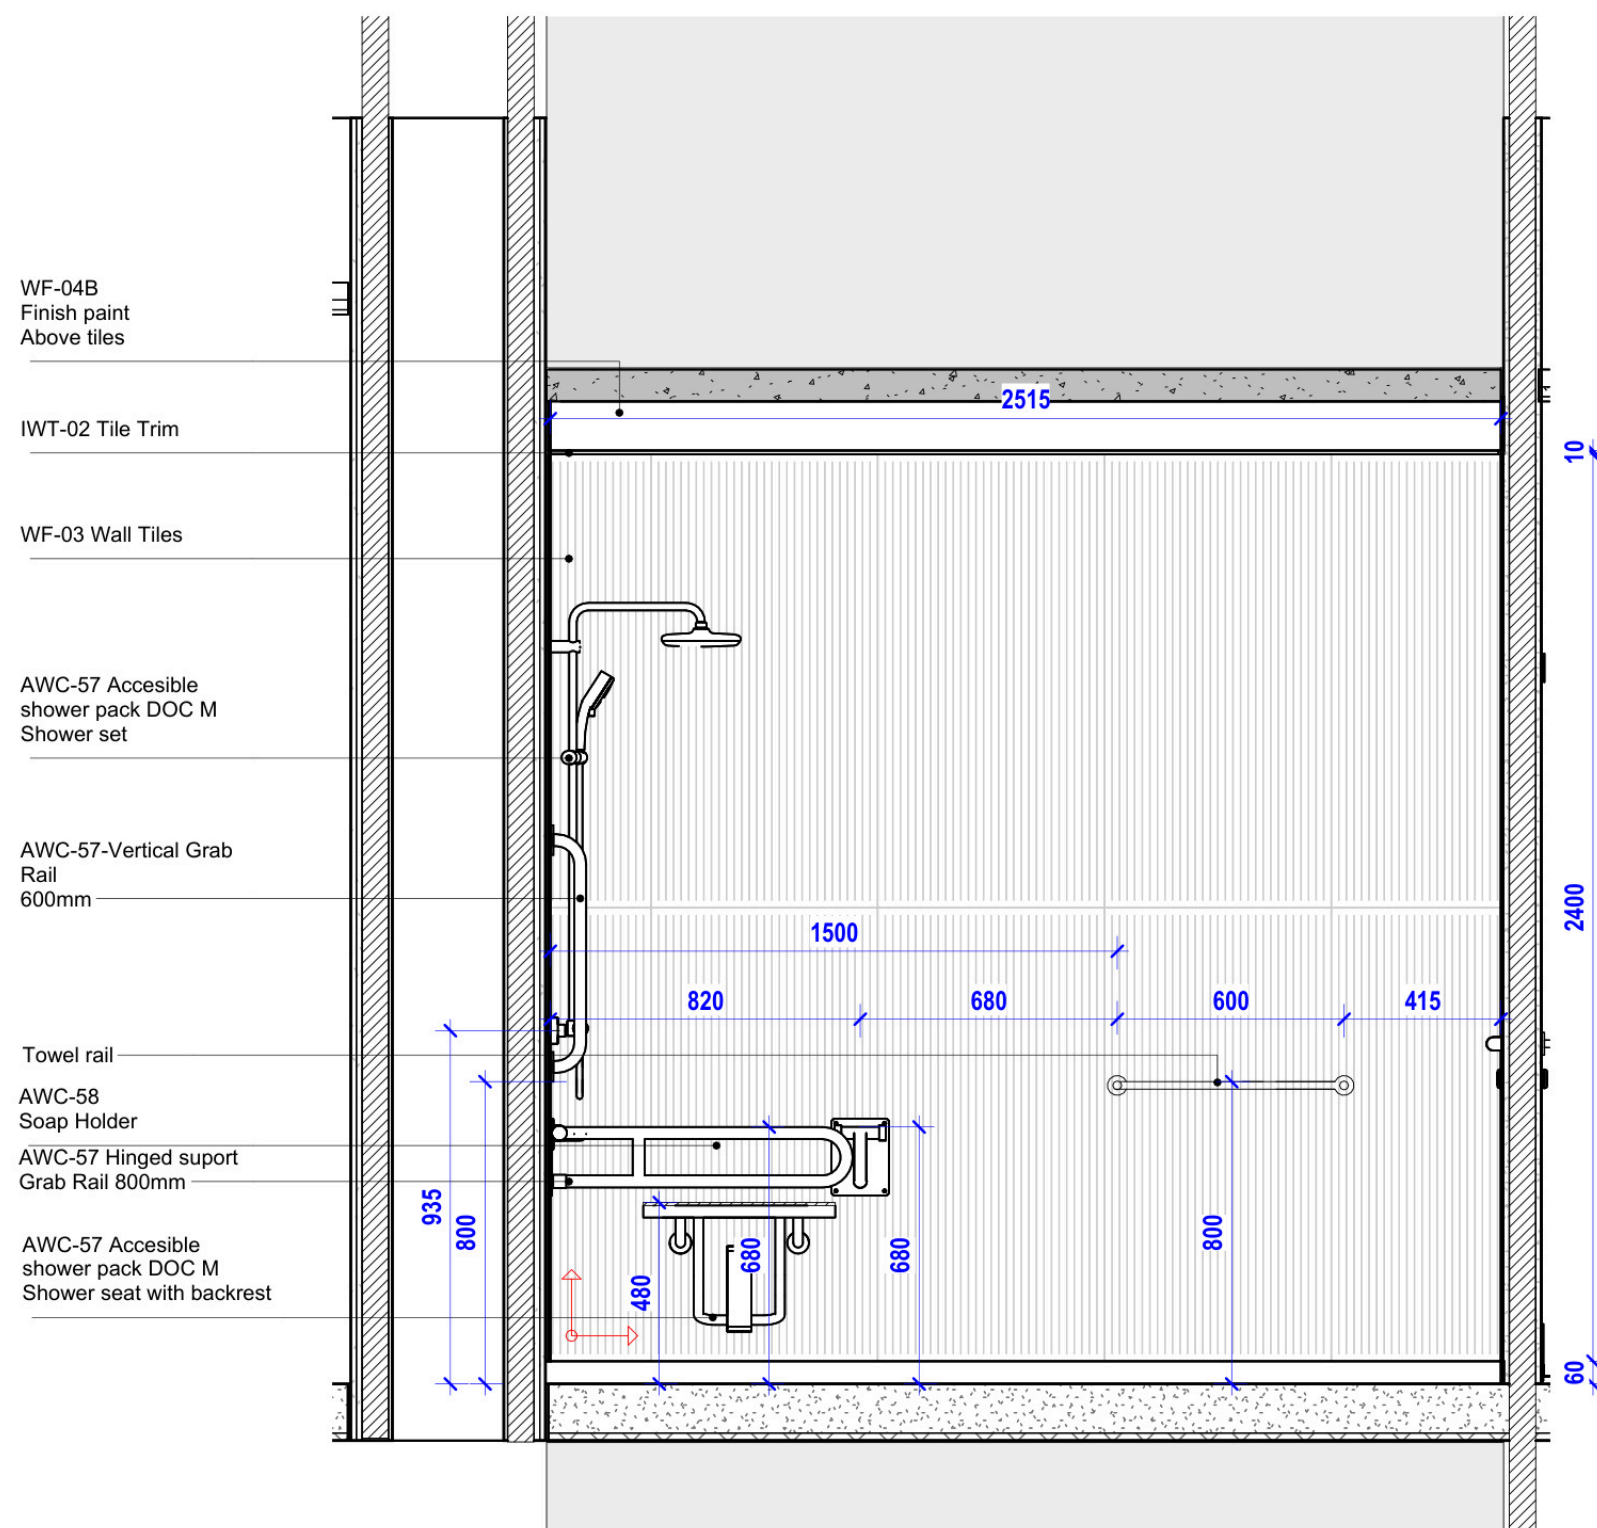

Ambulant Shower & WC Elevation -a1
1 : 20

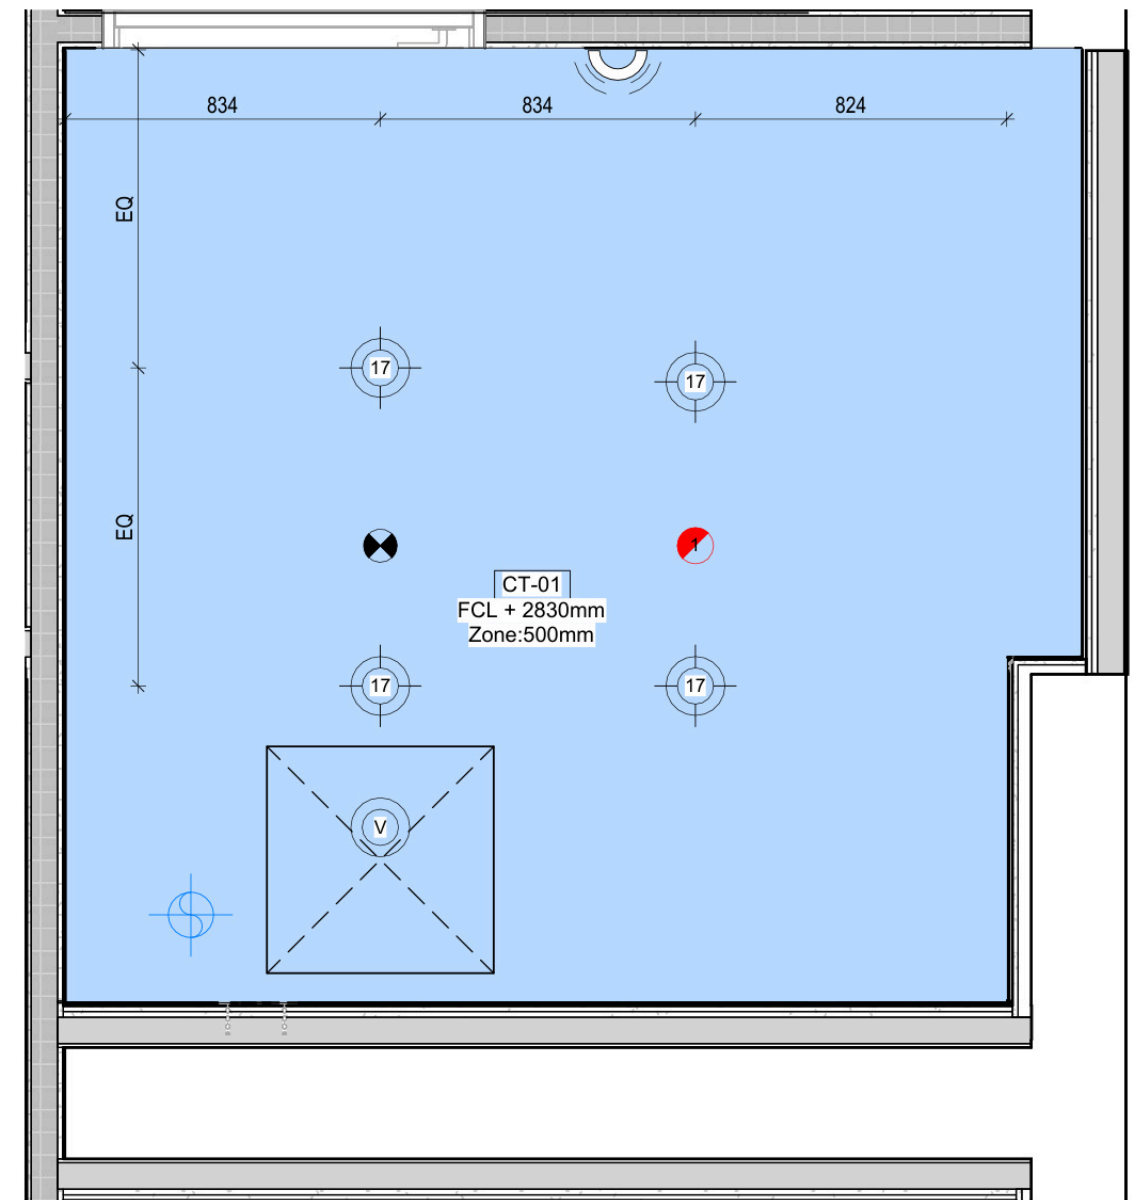

Ambulant Shower & WC B1 RCP
1 : 20

Zone = from finish ceiling height to underside of the slab
SE slab edge, beams

Ceiling Legend

Drawing Notes:

Electrical Syrn

- LED Recess
- LED Recess
- LED Recess
- LED Recess
- LED Decora
- Ceiling Mour
- AL13 - Cellir
- AL14 - Cellir
- AL15 - Cellir
- AL16 - Cellir
- AL17B IP R/
- AL23 -
- B3 - Ceiling
- E - Linear Str
- H - Linear Str
- D - Recessed
- W - Linear Str
- AL21 - Wall
- AL22 - Wall
- ALJ - Wall M
- AL23 - Wall H
- Manual Call
- Smoke Dete
- Smoke Dete
- Smoke Dete
- Fire Alarm S
- Green Break
- Security Car
- Emergency I

Mechanical

- Circular Extr
- Linear Suppl
- Linear Extra