


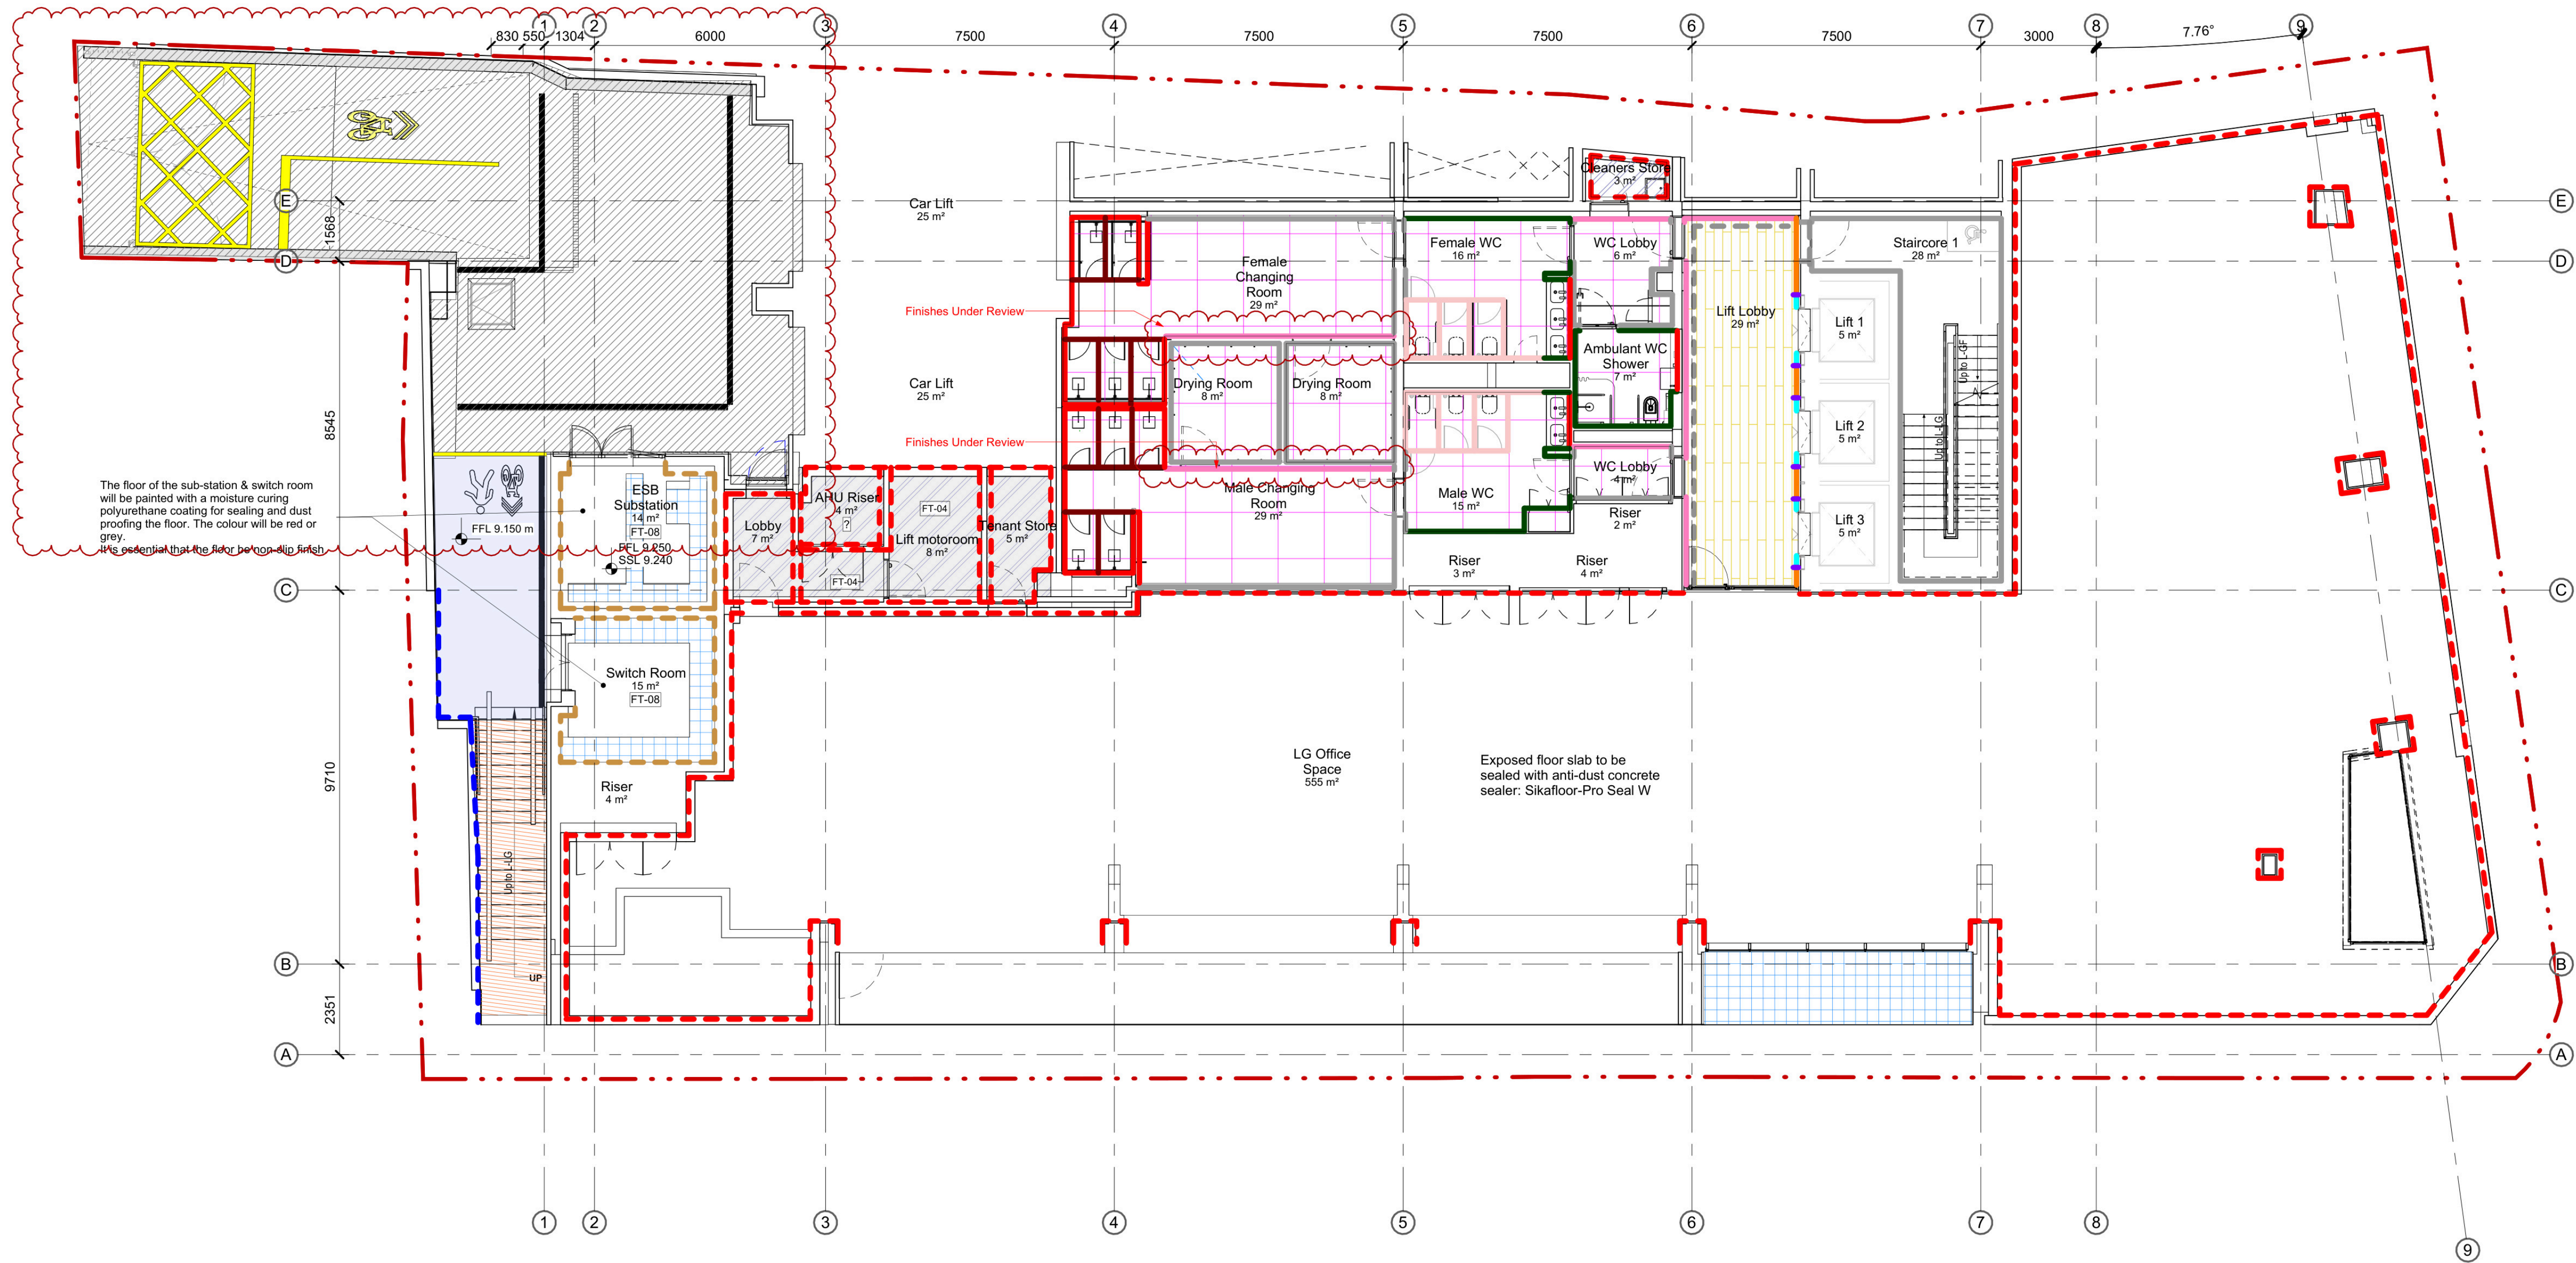

Floor Finishes:		Refer
IFF-0	1200	IFF-0
IFF-0	CANI	36+ \
IFF-0	finish	finish
IFF-0	Tufting	(TBC inten)
Finist		Finist
45-3C	gratin	Press finish
Wato	baser	Wato
Wato	solid and li	Wato
Wato	solid and li	Wato
Wato	Marki	Wato
paint	white strips	paint
Wall Finishes:		Ver
WF-01		Ver
WF-02		Ac
WF-03		Liv
WF-04		Aq
WF-05		Pai
WF-06		Pai
WF-07		nAt
WF-08		Aq
WF-09		Ver
WF-10		TCI
WF-11		Bau
WF-12		TCI
WF-12		Bro
WF-14		Typ
WF-15		Pair

General Notes:

- Refer to architects spe
- Refer to architectural fi
- Refer to interior archit
- Refer to window curtai
- Refer to window and screen
- Refer to door schedule
- Refer to PTN drylining
- Refer to all other consi
- Refer to all other consi
- Refer to all other consi
- All Dimensions to be v