


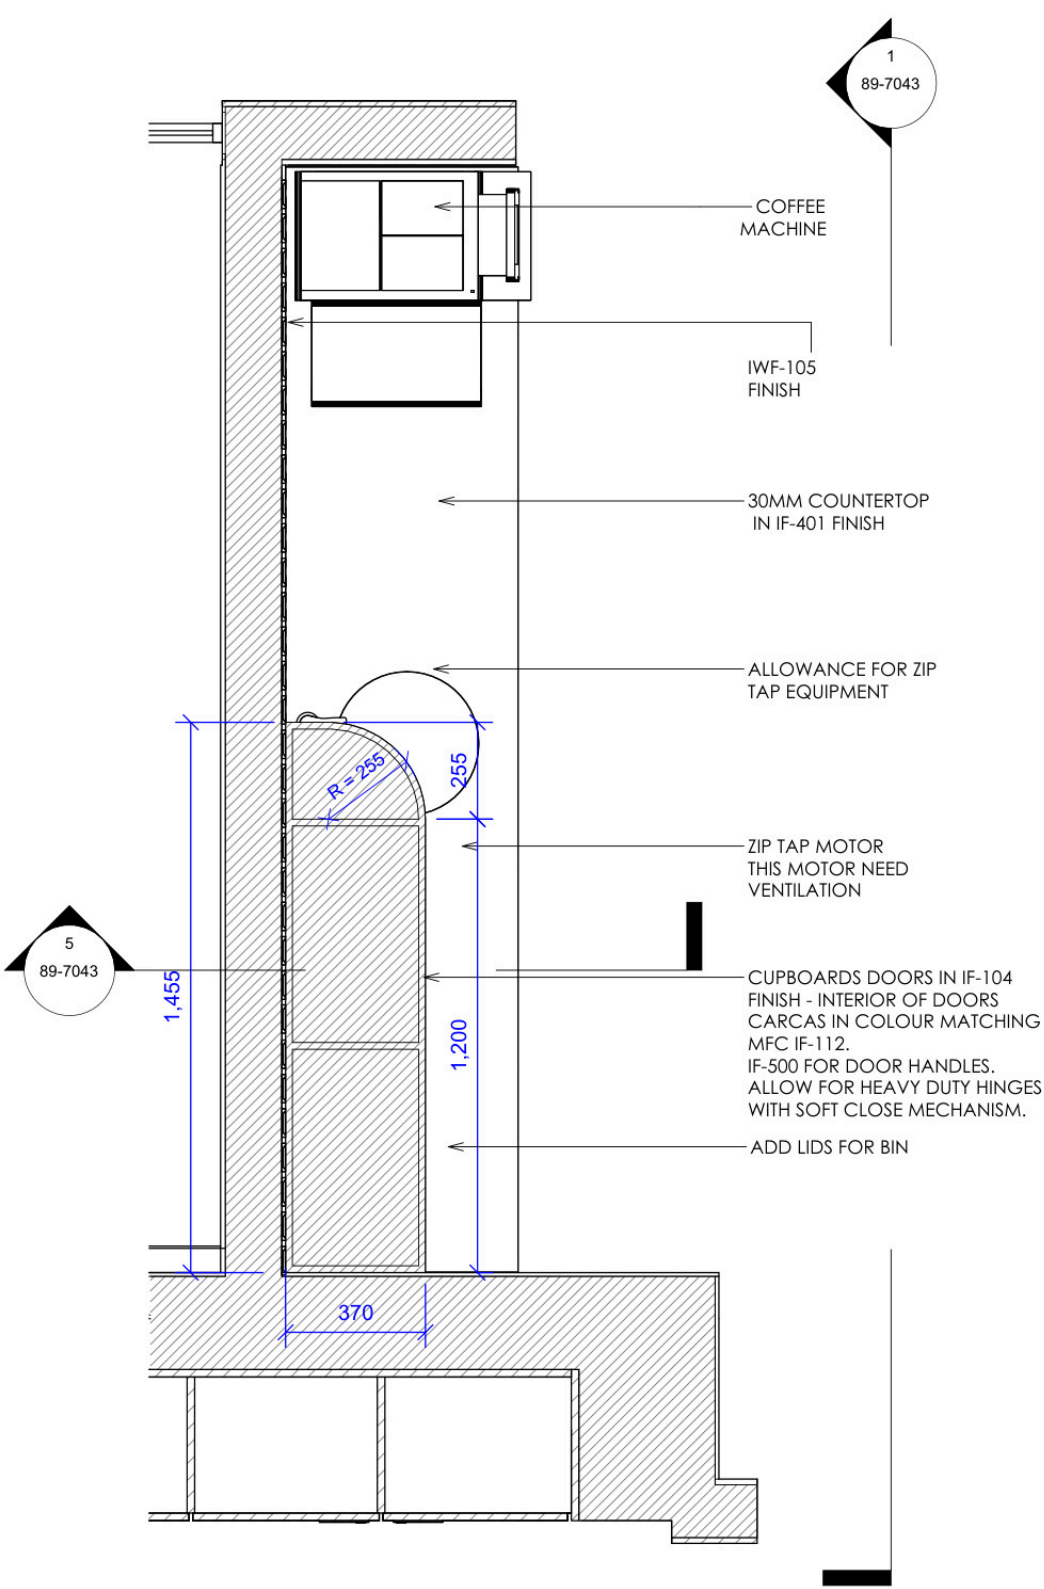


PULL OUT BIN




SINK REFERENCE- EDGE SINK UNDERMOUNT & REBATED INTO THE WORKTOP. SPEC TO BE PROVIDED BY JOINER FOR APPROVAL.


Tea Station - Schedule			
Type Mark	Count	Description	Floor Level
JY6-09	1	Tea Station 6th Floor	6th Floor

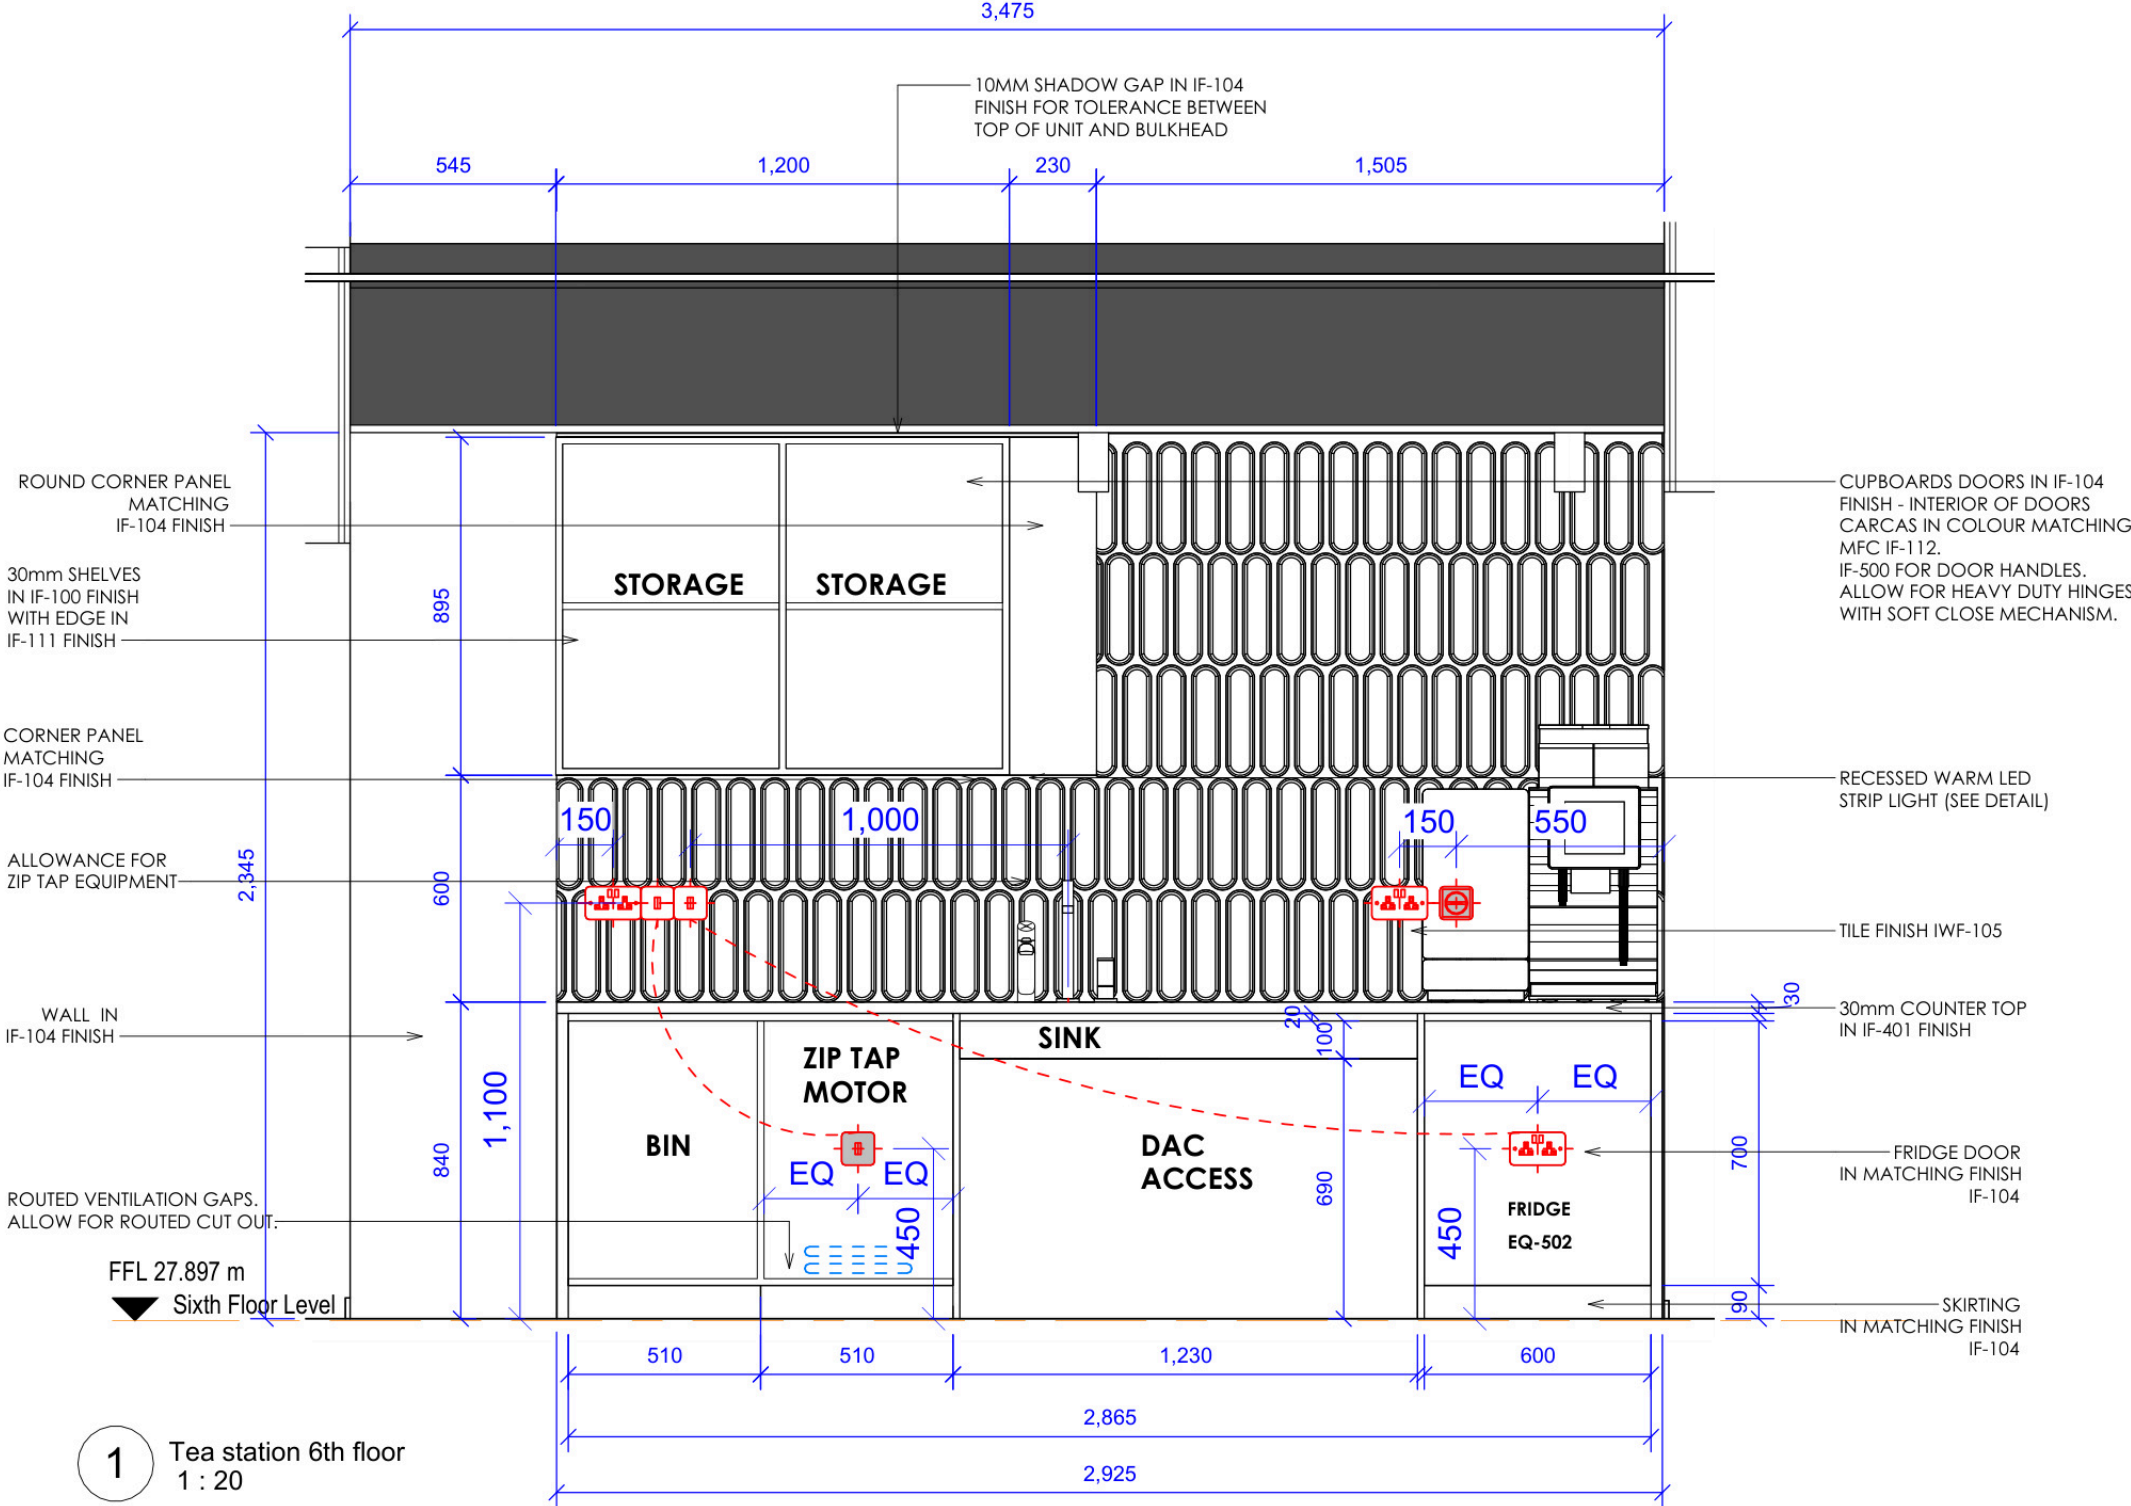


1 Tea station 6th floor
1 : 20

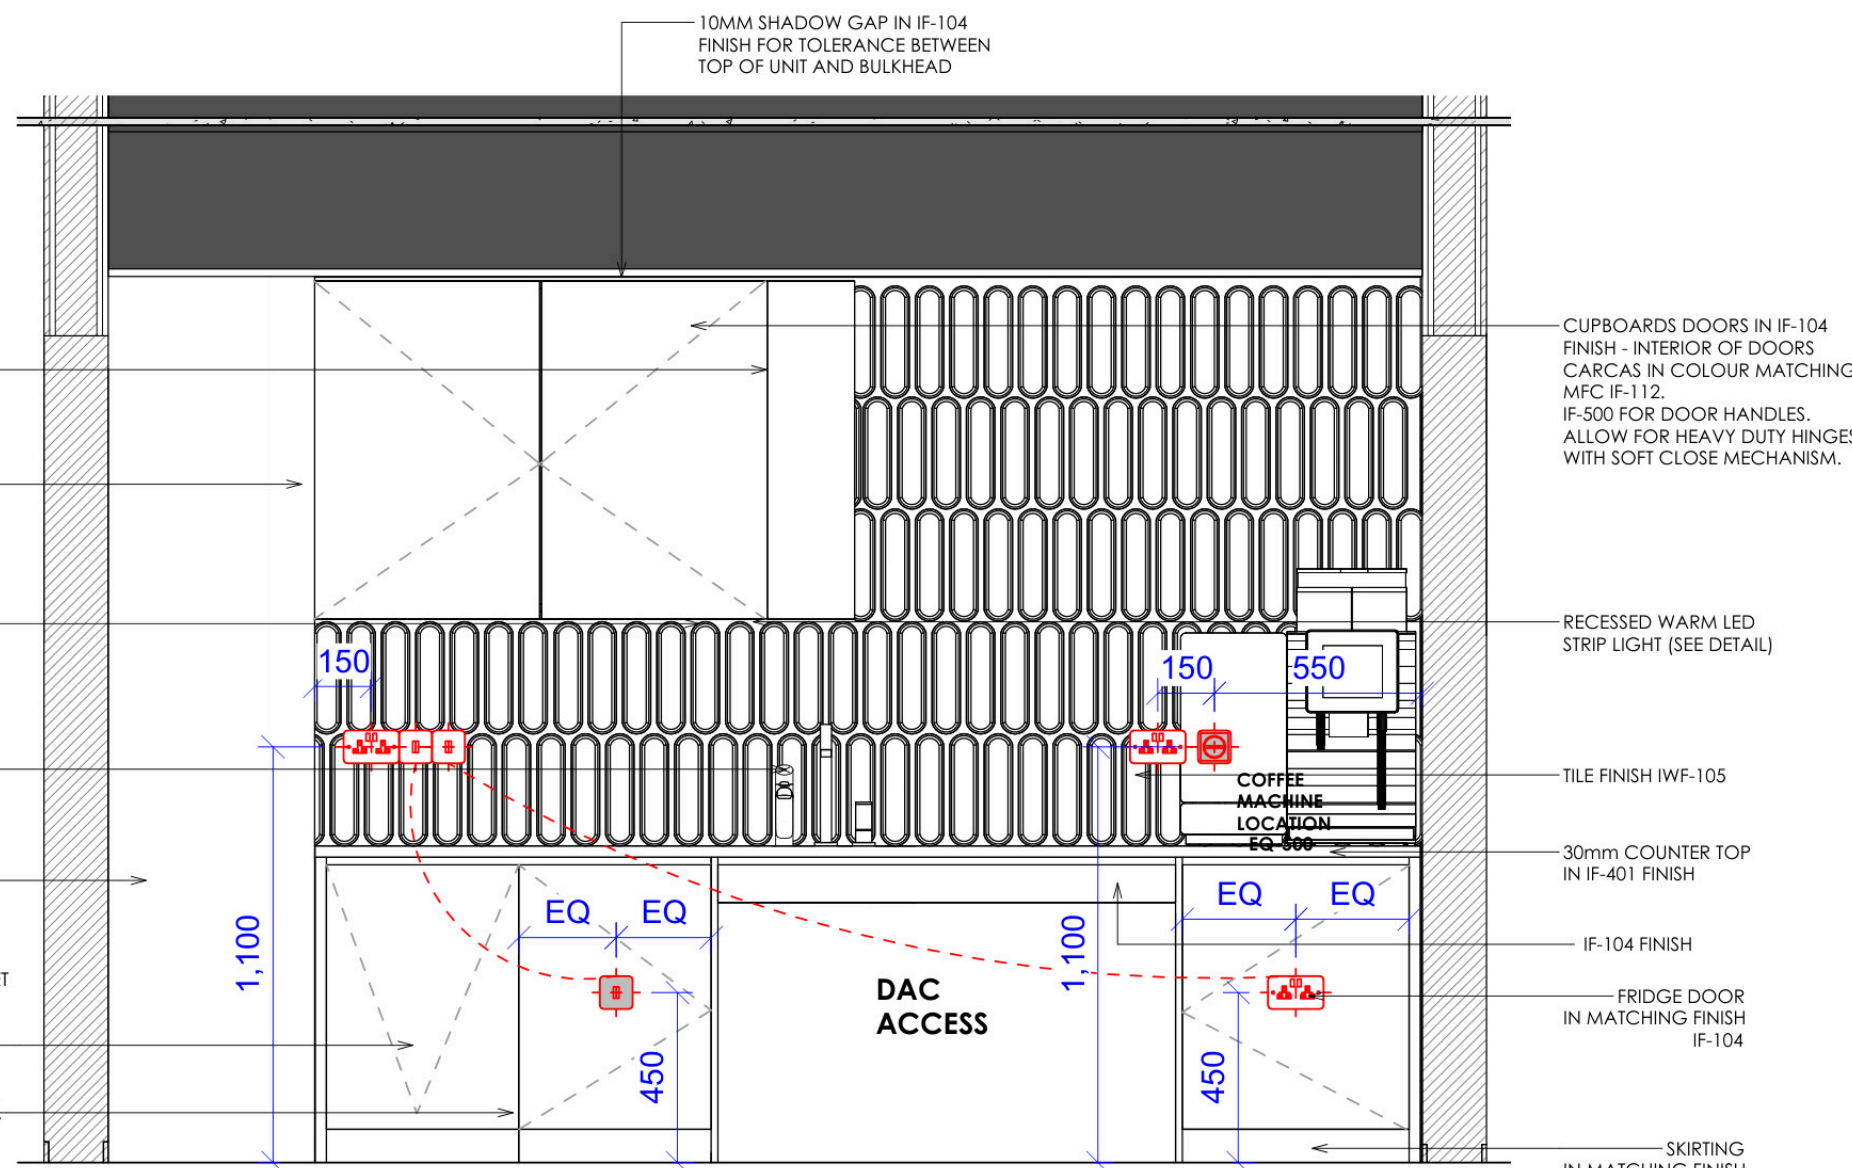


4 L06-Typical Floor Front Elevation Tea Station 6th floor
1 : 20

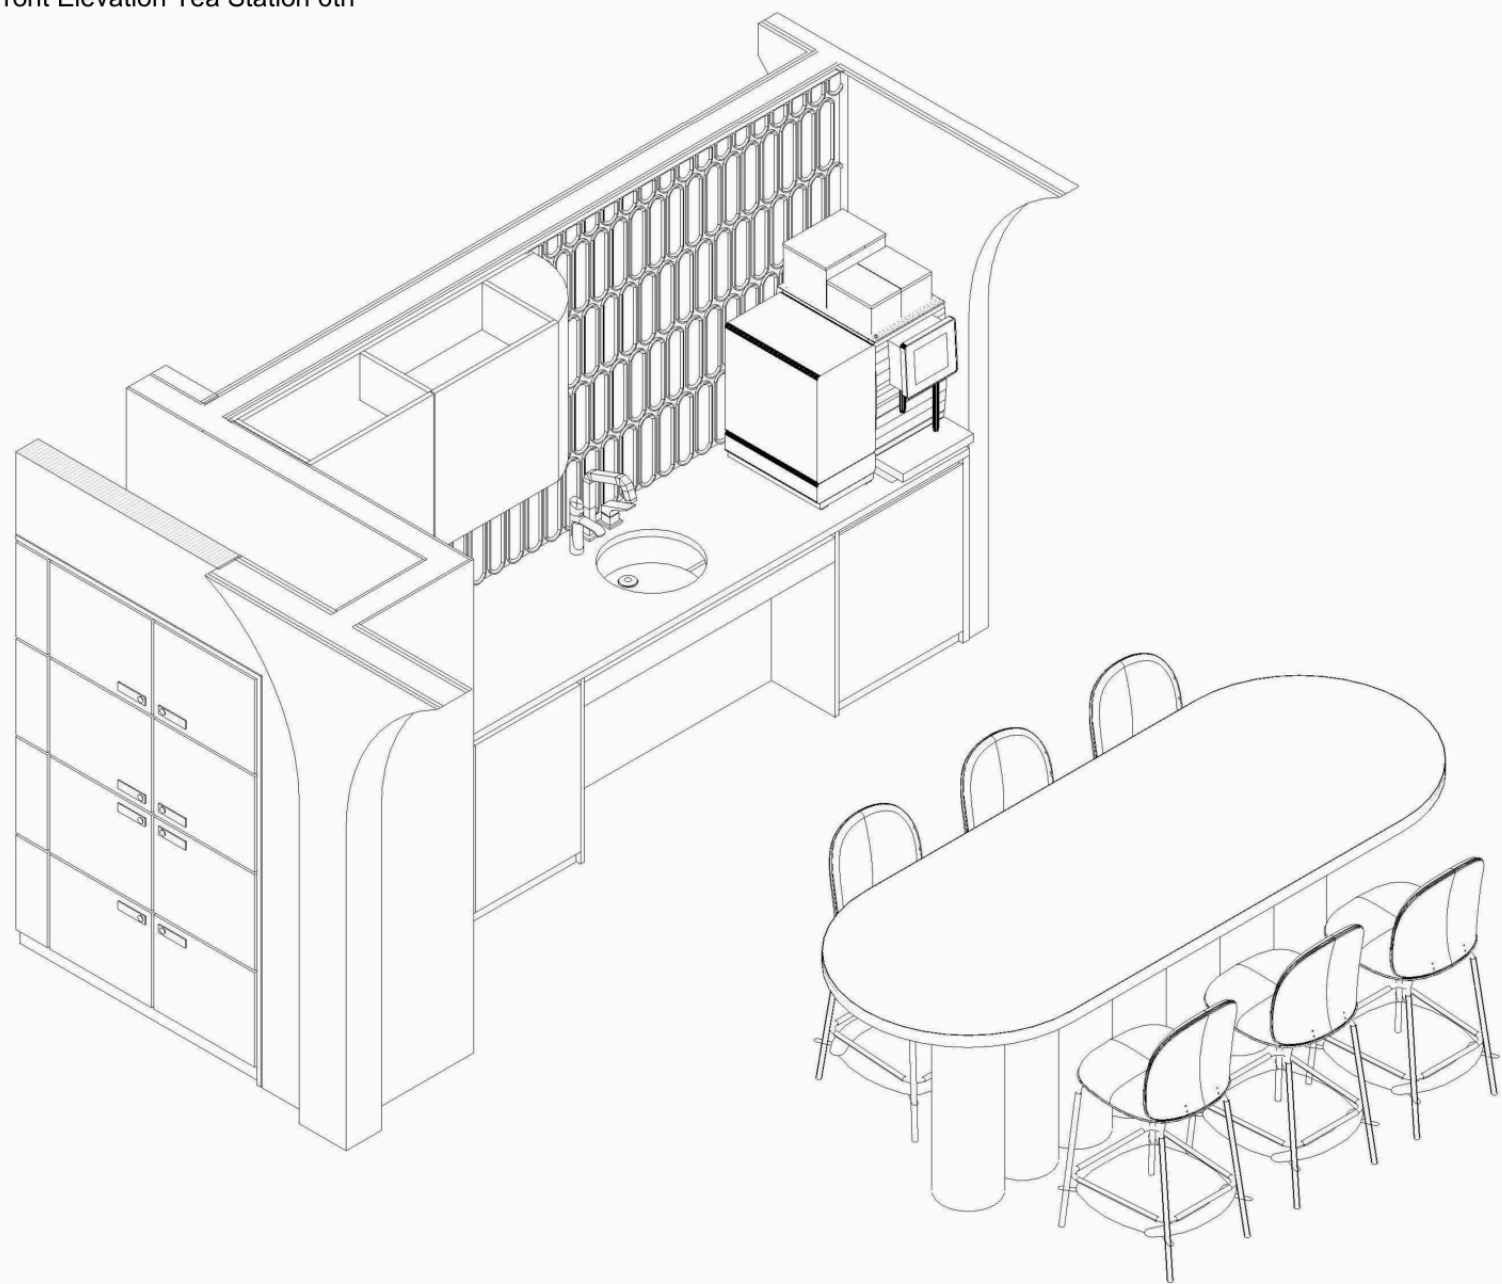


3D IMAGE - FOR REFERENCE ONLY

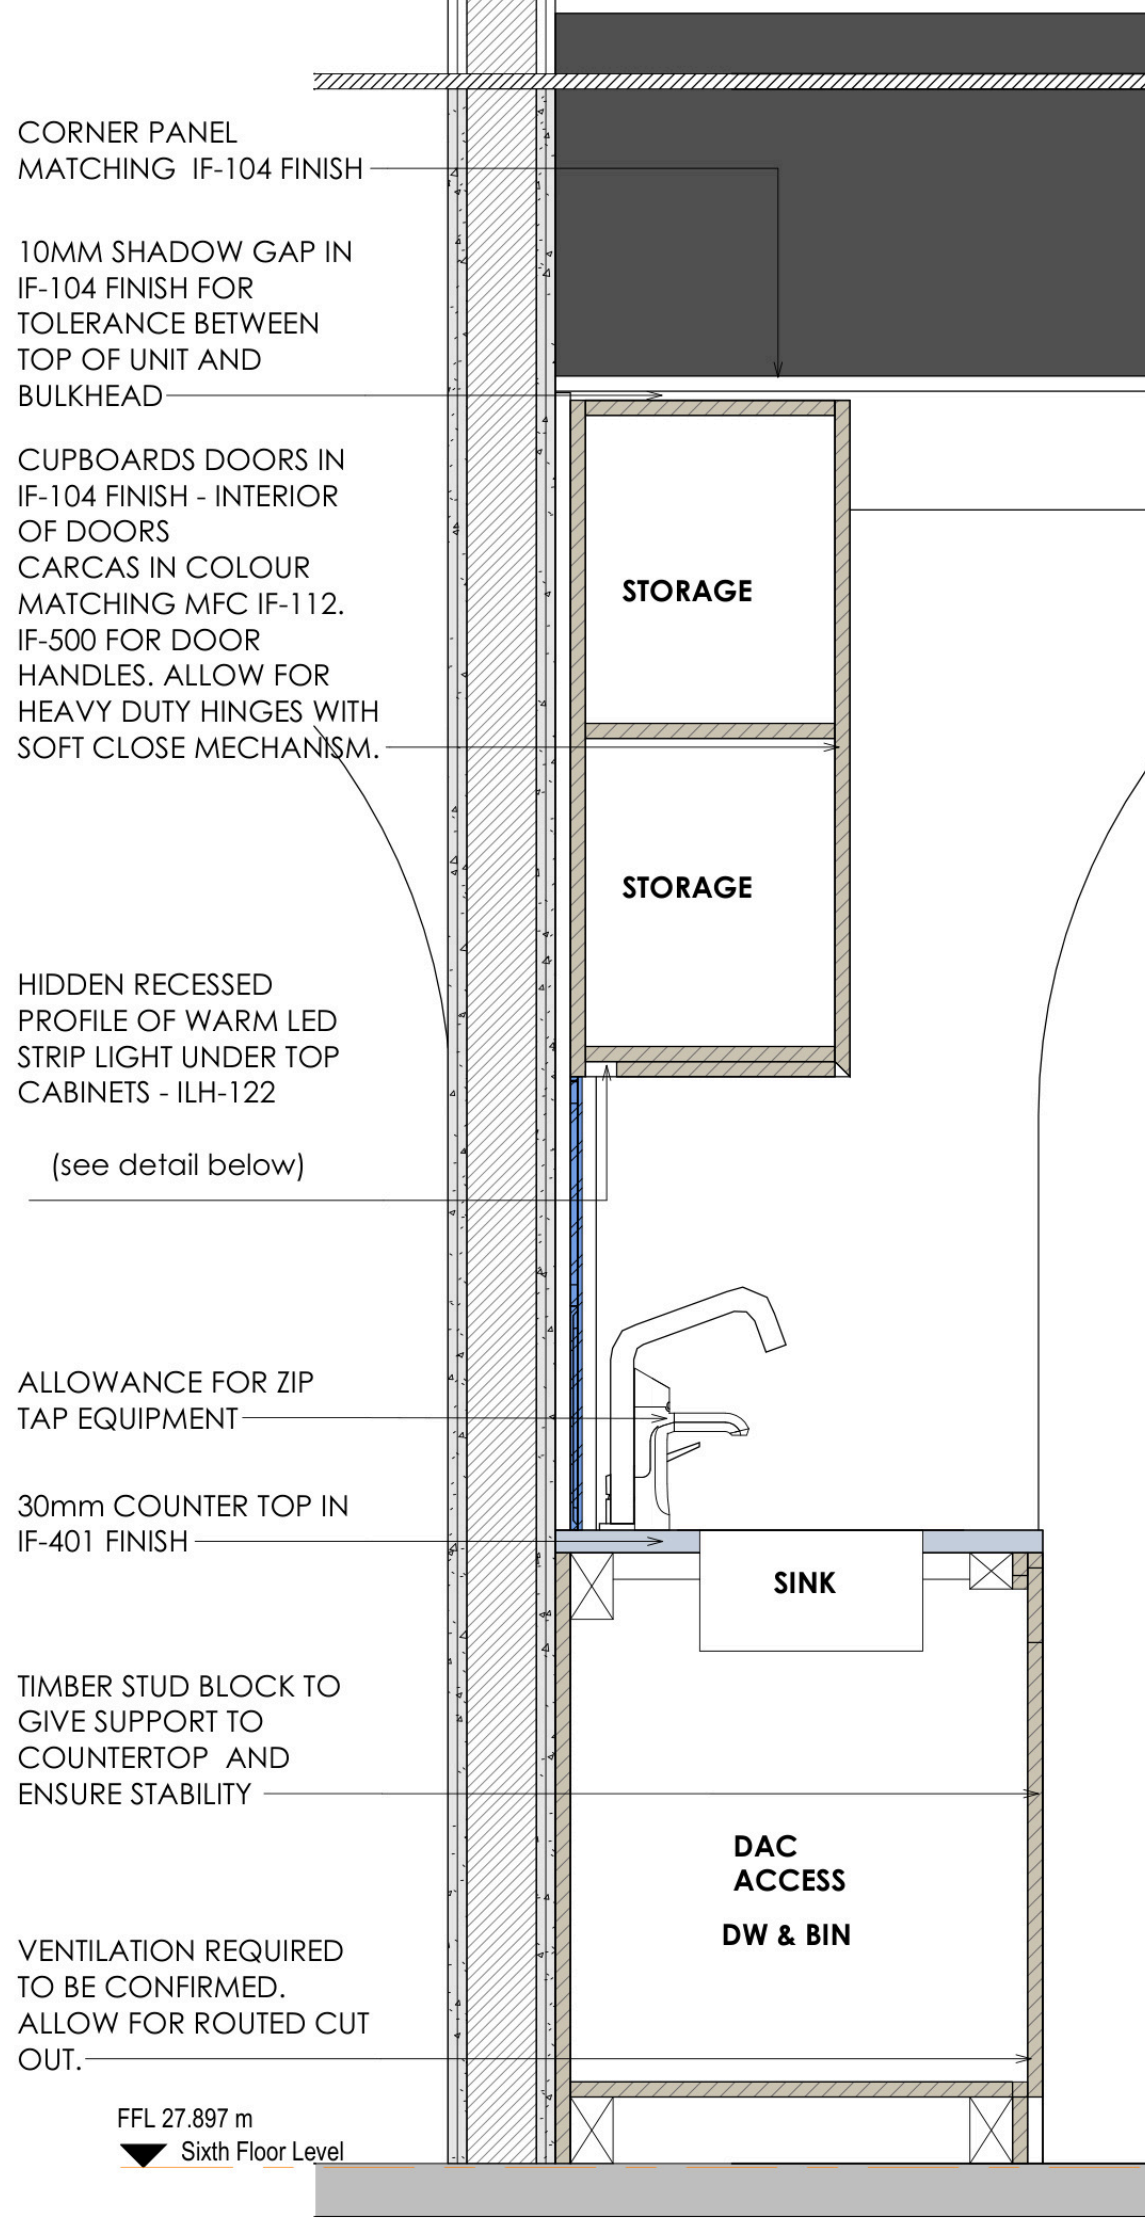

5 L06-Typical Floor Section Tea Station 6th floor
1 : 10

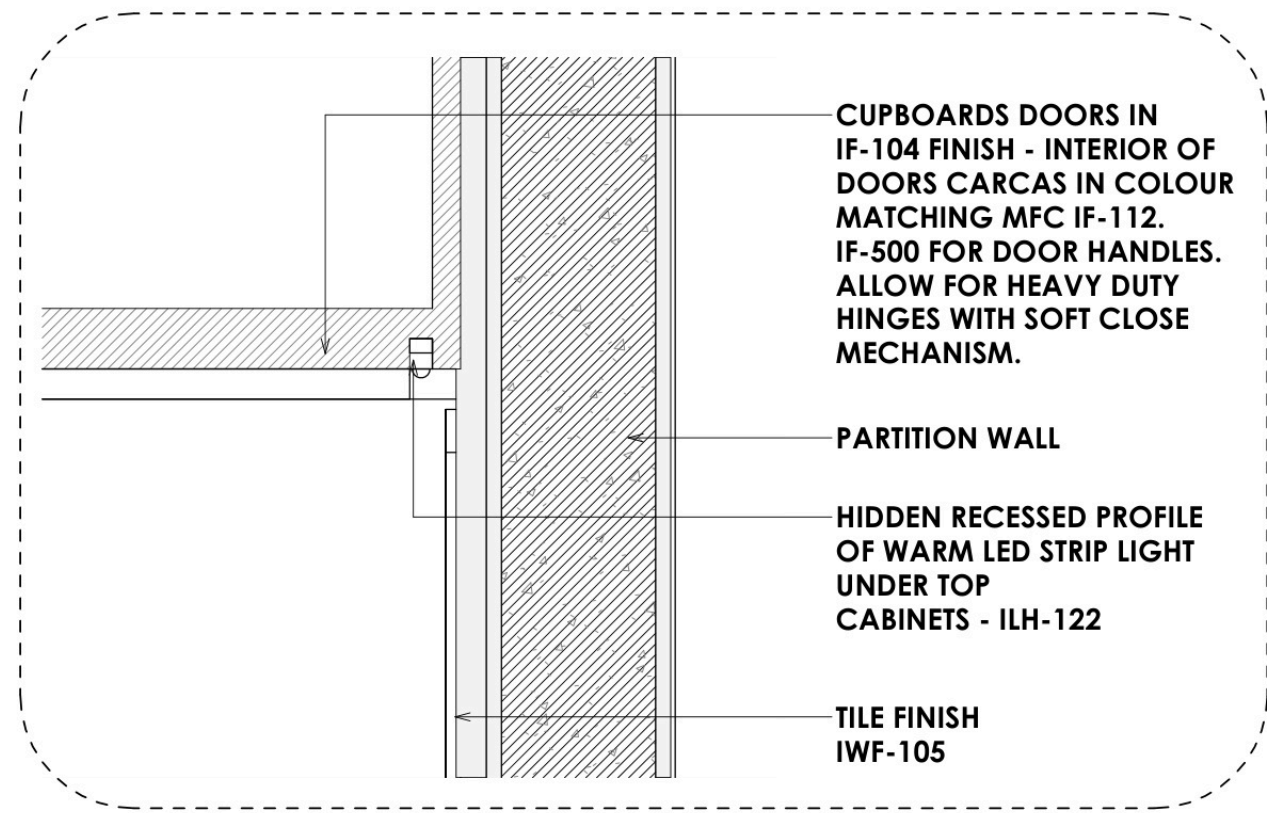

3 L06-Typical Floor Tea Station 6th Floor
1 : 5

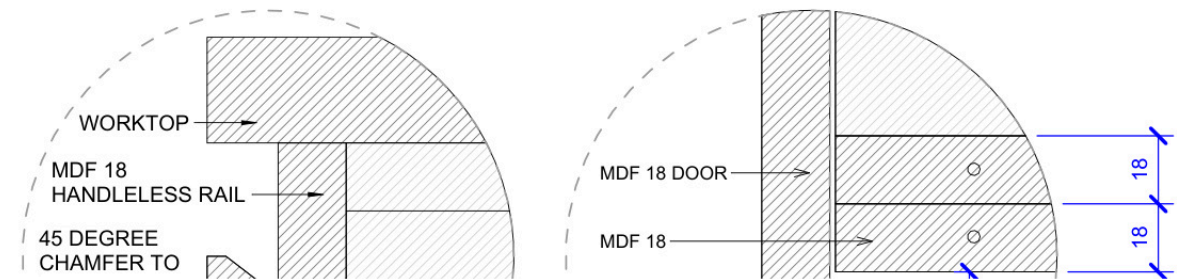

Drawing Notes:

General Note:

1. Shop Drawing to be approved/sign off before construction.
2. All existing dimensions including any loose floor are to be brought to the locations with reference to the existing structure.
3. All switch points are to be approved by the architect.
4. All drawings to be prepared in accordance with the specifications and present.
5. Samples for all finishes to be provided by the architect.
6. Part samples as per the architect's requirements.
7. Stability of the unit to be confirmed by the contractor/joiner.
8. Please read all drawings and specifications before construction.
9. Joiner to conduct the work.
10. Part samples to be provided by the architect.
11. All timber/mdf to be approved by the architect.

Electrical Symbols

	Two Way Switch
	Two Way Switch with Indicator
	Isolator
	Fuse
	Isolator
	2 Way GIC Dis
	CA
	5A
	Thru

Refer to M&E Consult information on spec